DIAGRAMA UNILINEAL

SIN ESCALA

NOTA:
- LOS MATERIALES QUE REQUIEREN CERTIFICACION PARA SU USO, CUMPLEN CON ESTE REQUISITO.

EMPALME SUGERIDO
A9-8,80-10,0 KVA (40 A)
PROTECCION EN
EQUIPO DE MEDIDA

CONECTADA A
1 X BARRA COPPERWELD
5/8" X 1.5 m
S: 8.37 mm2
D: PVC 32 mm
MEDICION DE PUESTA A TIERRA
TELUROMETRO: FLUKE 1630
No. SERIE: 29650078-C

Rmedida = x ohm

CONECTADA A
1 X BARRA COPPERWELD
5/8" X 1.5 m
S: 8.37 mm2
D: PVC 32 mm
MEDICION DE PUESTA A TIERRA
TELUROMETRO: FLUKE 1630
No. SERIE: 29650078-C

Rmedida = x ohm

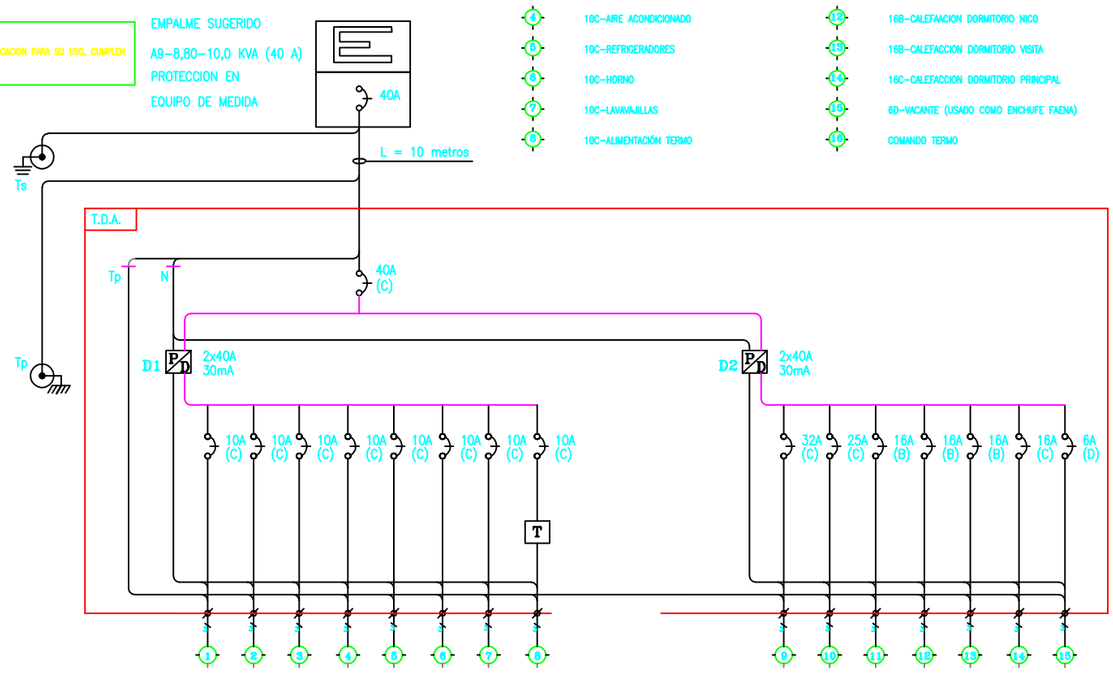

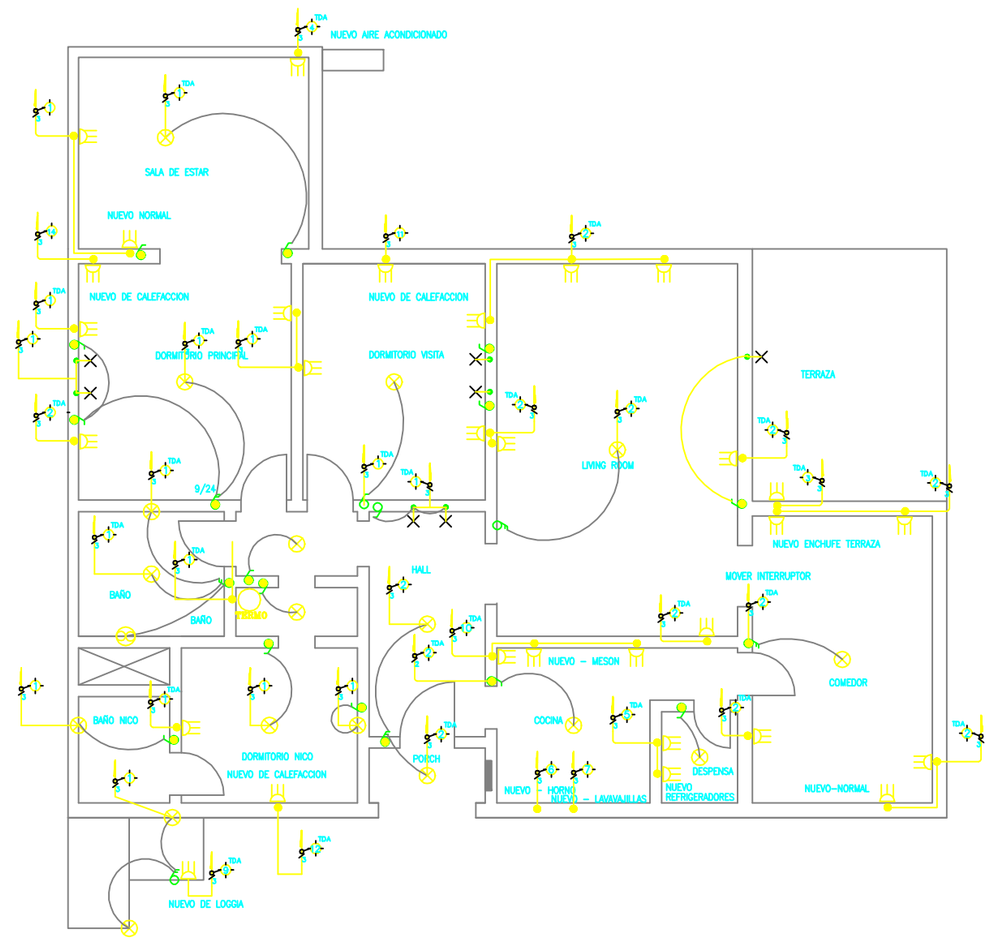

SIMBOLOGIA

- ENCHUFE TRIPLE 10(A)-220(V).- SOBREPUESTO
- ENCHUFE TRIPLE 10(A)-220(V).- EMBUTIDO EN CAJA DE DISTRIBUCION
- CAJA PVC DE DISTRIBUCION 1/2"Ø
- EXTRACTOR DE AIRE
- CAJA DE CONEXION
- APLIQUE
- SOQUETE P/FOCO INCANDESCENTE 100W
- CAJA PVC DE DISTRIBUCION 1/2"Ø
- INTERRUPTOR 9/12
- INTERRUPTOR 9/15
- TABLERO DE DISTRIBUCION ALUMBRADO Y ENCHUFES

CONTENIDO: PLANTAS, DIAGRAMA UNILINEAL Y CARGAS

PRESUPUESTO 953

alectrico

UBICACION

INSCRIPCION SEC

N

INSCRIPCION SEC N°

FECHA:

AMPLIACION ELECTRICA VIVIENDA

UBICACION: PROFESOR RODOLFO LENZ 502
COMUNA: ÑUÑOA

LAMINA: 1 DE 1
ESCALA: 1: 100
FECHA: 6/2018

PROPIETARIO:
DOÑA LIDIA VALENZUELA
RUT: 1.X

INSTALADOR:
A. ESPINOSA HERNANDEZ
INST. ELECTRICO CLASE D
REG. SEC. 14.579.554-0